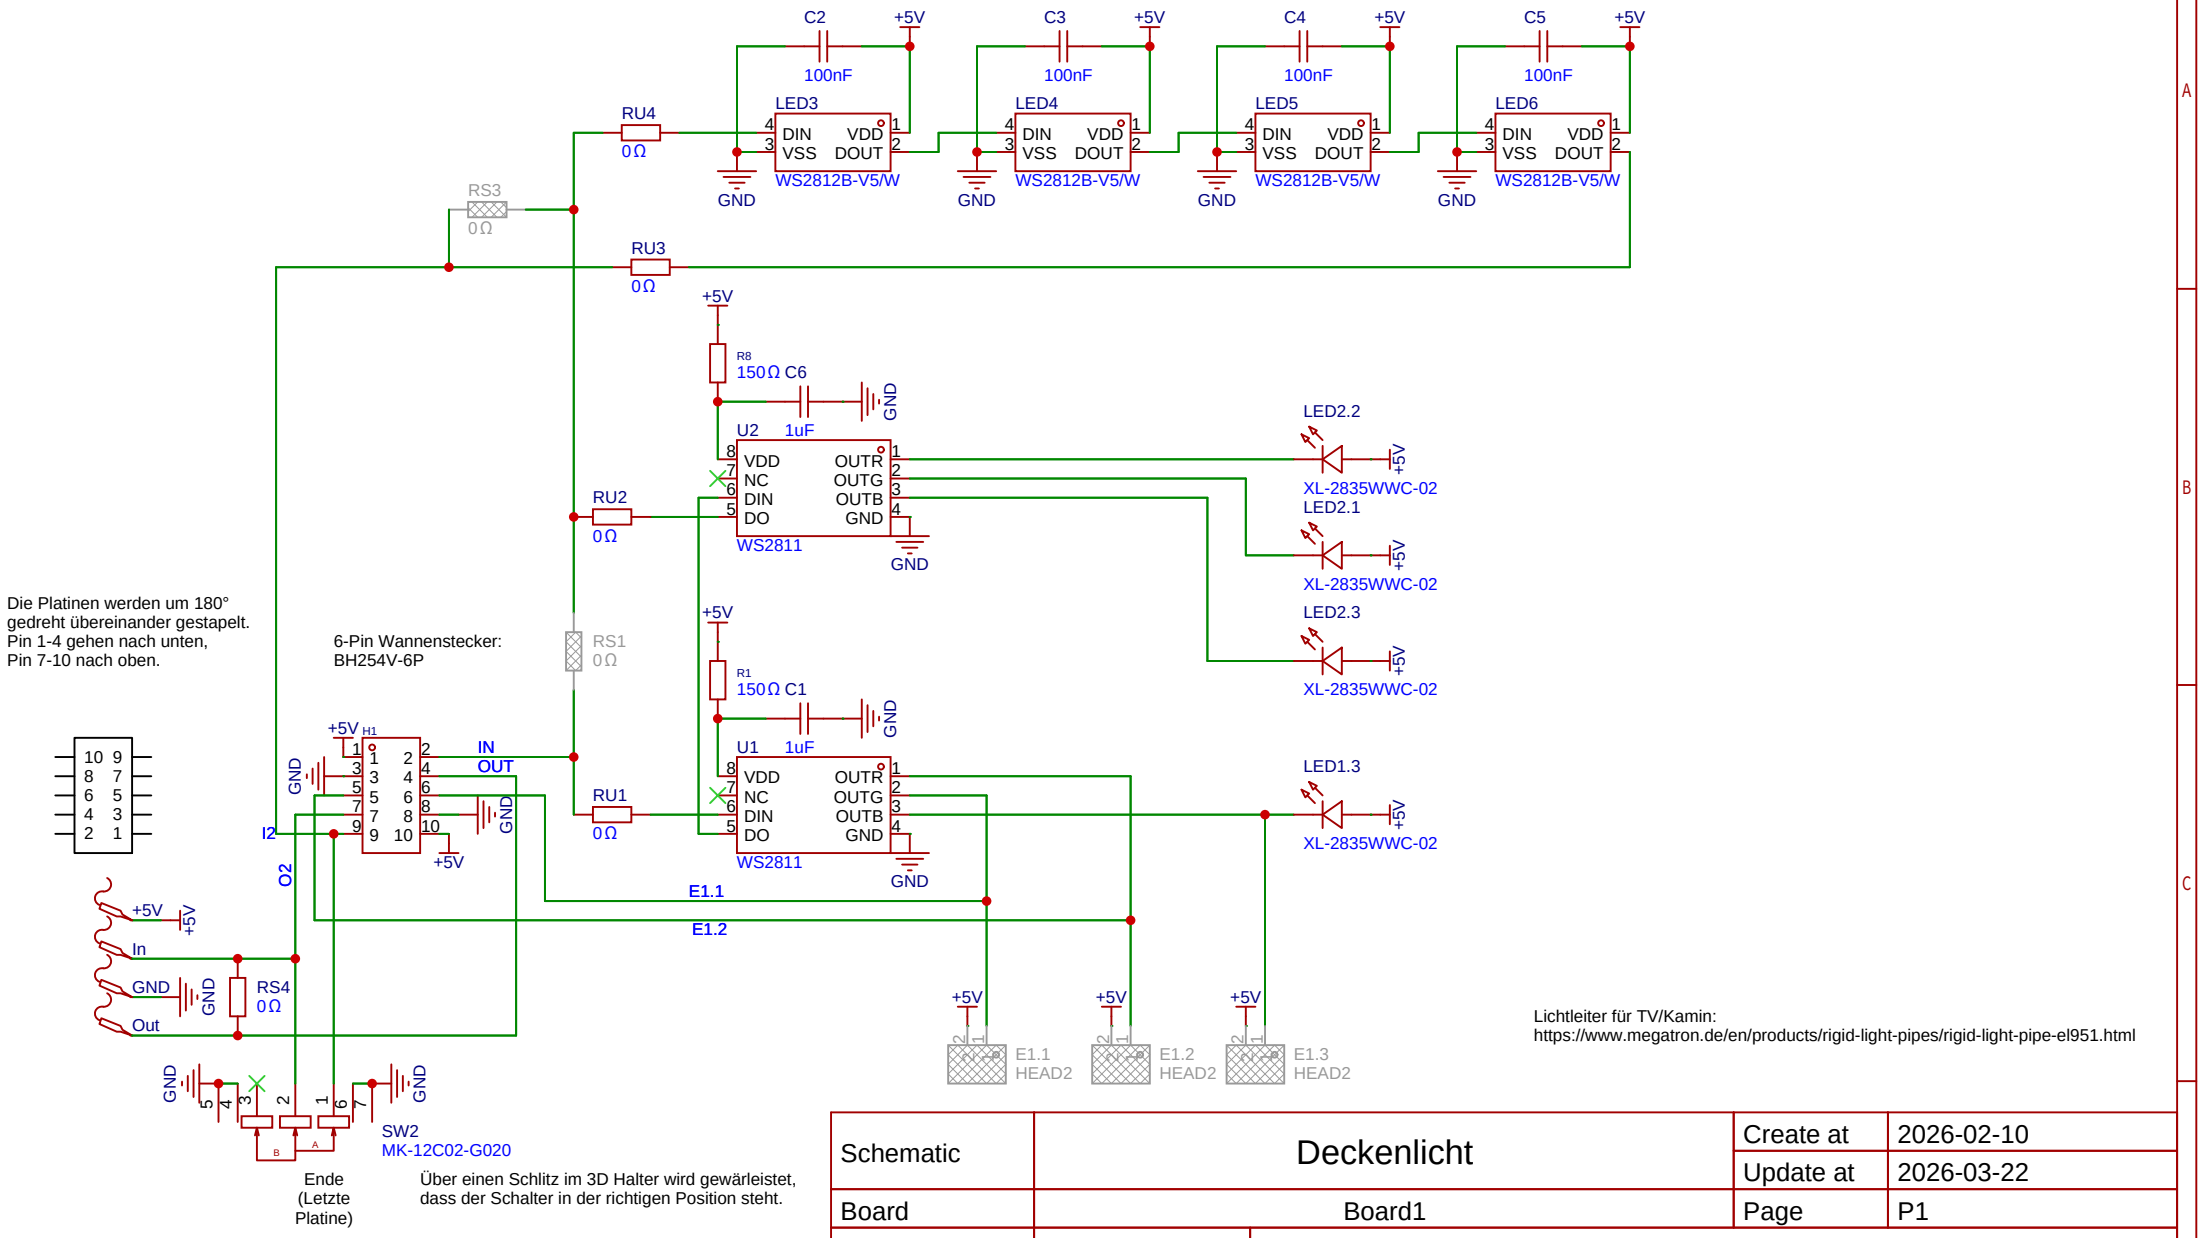

Lichtleiter für TV/Kamin:
https://www.megatron.de/en/products/rigid-light-pipes/rigid-light-pipe-el951.html

FALLER 130277 - Fachwerkhaus: 64 x 49 x 34
FALLER 131324 - Schwarzwälder Bauernhaus: 88 x 62 x 45

Stiftleisten:
2x2 Pol: https://de.aliexpress.com/item/1005010496849556.html
Länge: 13, 15, 17, 19, 21, 23, 25, 30, 35, 40, 45, 50

2x40 Pol: https://de.aliexpress.com/item/4000044912363.html
Länge: 20, 25, 30, 40, 45 (die letzten drei habe ich da)

Schematic	Deckenlicht	Create at	2026-02-10
		Update at	2026-03-22
Board	Board1	Page	P1
Drawn		Hausdeckenlicht	
Reviewed			
		Version	Size / Page 1 Total 1
EasyEDA		V1.1	A4 / EasyEDA.com